



N:\2022\022-041A - Colton - Lot 15, Pine Canyon\3D\Revit\Drawings\Colton - Camiloli.rvt 9/7/2022 11:32:43 AM

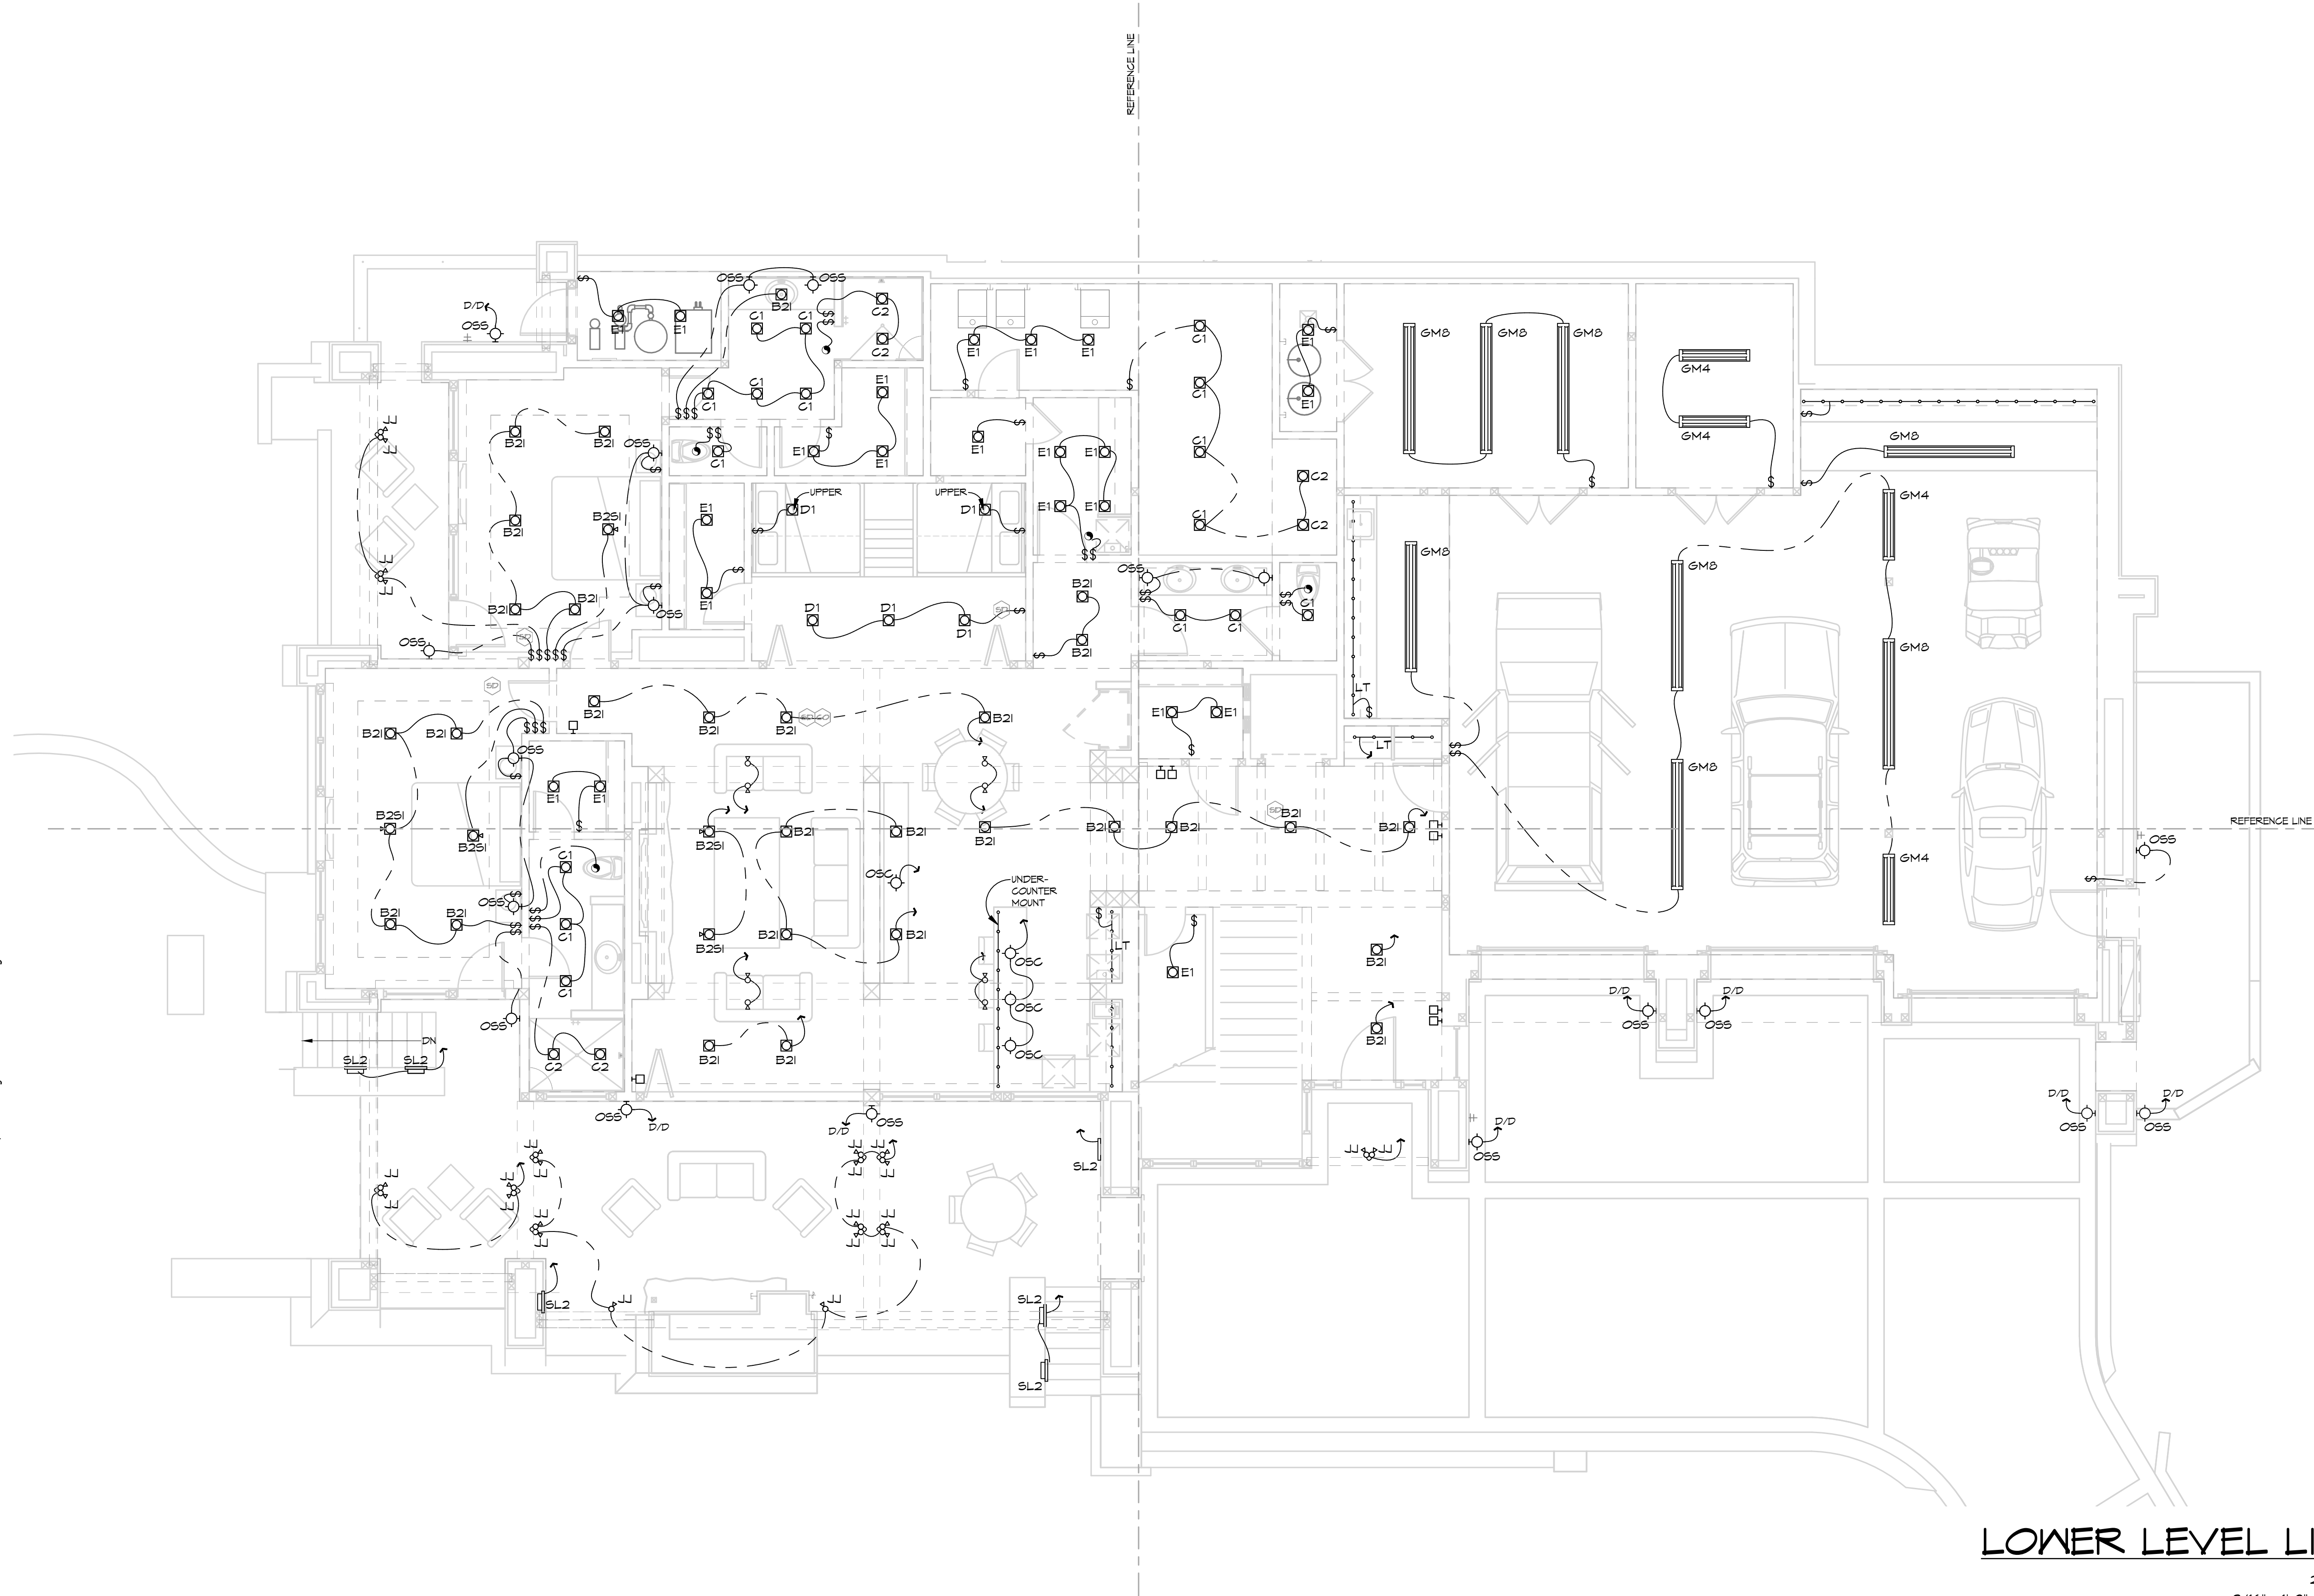

## LOWER LEVEL LIGHTING PLAN

3/16" = 1'-0"  
SCALE  
2 0 2 4 6 8 10 12 14  
FEET

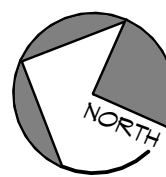

| ELECTRICAL SYMBOL LEGEND |                                                                          |
|--------------------------|--------------------------------------------------------------------------|
|                          | SWITCH SINGLE POLE @ 148" A.F.F. UNLESS NOTED OTHERWISE                  |
|                          | 3 WAY SWITCH                                                             |
|                          | 4 WAY SWITCH                                                             |
|                          | SMART SWITCH                                                             |
|                          | DIMMER SWITCH                                                            |
|                          | DOOR JAMB SWITCH                                                         |
|                          | LIGHT, C.L.G. MOUNTED                                                    |
|                          | LIGHT, C.L.G. MOUNTED                                                    |
|                          | LIGHT/WALL MOUNTED @ 40" UNLESS NOTED OTHERWISE                          |
|                          | LIGHT,SURFACE MOUNTED ADJ. SPOT                                          |
|                          | FIRE SPRINKLER ALARM                                                     |
|                          | LIGHT, RECESSED IN CEILING                                               |
|                          | LIGHT, RECESSED IN CEILING (ADJUST.)                                     |
|                          | LIGHT, RECESSED WALL WASHER                                              |
|                          | STRIP LIGHTING                                                           |
|                          | LIGHT RECESSED IN WALL @ 12" UNLESS NOTED OTHERWISE                      |
|                          | FLUORESCENT LIGHT,SURFACE MTD. UNLESS NOTED OTHERWISE                    |
|                          | FLUORESCENT WALL MOUNT (ABOVE DOOR)                                      |
|                          | PLASTER WALL SCONCE @ 10" UNLESS NOTED OTHERWISE                         |
|                          | WEATHER PROOF LIGHT FIXTURE LISTED FOR DAMP LOCATION                     |
|                          | "J-BOX" FLUSH MOUNTED                                                    |
|                          | MULTI SPEED FAN, 2 CIRCUITS, DBL. SWITCH                                 |
|                          | POWERSTRIP IN DRAWER POWER FROM GFCI RECEPTACLE @ 12"                    |
|                          | 110V DUPLEX RECEPTACLE MOUNTED AT POTSHELF LEVEL                         |
|                          | DUPLEX 110V RECEPTACLE @ 12" UNLESS NOTED OTHERWISE                      |
|                          | FOURPLEX 110V RECEPTACLE @ 12" UNO                                       |
|                          | RECEPTACLE @ 12", ONE SIDE SWITCHED                                      |
|                          | 220 VOLT RECEPTACLE                                                      |
|                          | RECEPTACLE WITH GROUND FAULT INTERRUPTER (GFCI), MTD. ABOVE COUNTER      |
|                          | ENTIRE CIRCUIT SHALL BE PROTECTED BY AN ARC-FAULT CIRCUIT INTERRUPTER(S) |
|                          | RECEPTACLE WEATHERPROOF, GFCI                                            |
|                          | CLOCK BOX                                                                |
|                          | GFCI RECEPTACLE RECESSED IN FLOOR, VERIFY LOCATION                       |
|                          | TELEPHONE JACK                                                           |
|                          | PHONE JACK, RECESSED IN FLOOR                                            |
|                          | DATA JACK                                                                |
|                          | CABLE TV JACK                                                            |
|                          | CABLE TV JACK, FLOOR MOUNT                                               |
|                          | PUSH BUTTON/DOOR BELL                                                    |
|                          | CHIME                                                                    |
|                          | EXHAUST FAN TO OUTSIDE, 5 AIR CHANGES/HR. MIN.                           |
|                          | SPEAKER                                                                  |
|                          | THERMOSTAT                                                               |
|                          | GFCI DISCONNECT                                                          |
|                          | SMOKE DETECTOR                                                           |
|                          | DRAPERY POCKET POWER & LOW VOLTAGE CONTROL, VERIFY SWITCHING             |
|                          | SECURITY KEY PAD                                                         |
|                          | ELECTRICAL SES PANEL, FLUSH MOUNT                                        |
|                          | ELECTRICAL SUB PANEL                                                     |
|                          | LOW VOLTAGE TRANSFORMER                                                  |
|                          | LIGHTING CONTROL PANEL                                                   |
|                          | LIGHTING ZONE                                                            |
|                          | LIGHTING CONTROL KEYPAD                                                  |
|                          | LIGHTING CONTROL, MULTIPLE KEYPADS                                       |
|                          | CARBON MONOXIDE DETECTOR                                                 |
|                          | INTERCOM SYSTEM                                                          |
|                          | REMOTE EXHAUST FAN W/ GRILLE NEAR FLOOR                                  |
|                          | CEILING MOUNTED EXHAUST FAN                                              |
|                          | EXHAUST FAN ON ROOF                                                      |
|                          | DUSK TO DAWN PHOTOCELL                                                   |
|                          | POT SHELF                                                                |
|                          | TOE KICK                                                                 |
|                          | UNDER COUNTER                                                            |
|                          | WATER PROOF FIXTURE                                                      |
|                          | DAMP PROOF FIXTURE                                                       |
|                          | AUTOMATIC GARAGE DOOR OPENER                                             |
|                          | HOME RUN TO LIGHTING CONTROL SYSTEM                                      |
|                          | INFRARED HEATER 220V                                                     |

A CUSTOM RESIDENCE PREPARED FOR  
MR. & MS. COLTON  
LOT #15

**URBAN DESIGN architecture**  
**ASSOCIATES LTD. AIA** 480-905-1212  
8150 N. 86TH. PLACE SCOTTSDALE, ARIZONA 85258

DWG BY: BO/CP  
DATE: 09/07/22

REVISIONS:  
04/14/22 C.O.F. A  
05/17/22 C.O.F. A

ALL REVISIONS AND CHANGES  
REPRESENTED BY THESE DRAWINGS  
ARE THE PROPERTY OF THE  
ARCHITECT AND WERE CREATED FOR  
THE PROJECT AND NOT FOR ANY  
MISUSE, REUSE, ALTERATIONS,  
ADDITIONS AND/OR DELETIONS OF  
THESE DRAWINGS ON THIS PROJECT.  
THE USER'S SOLE RISK AND WITHOUT  
LIABILITY TO URBAN DESIGN ASSOC.,  
LTD. IN THE EVENT OF ANY LOSS OR  
DAMAGE TO ANY ORIGINAL OR  
ELECTRONIC FILES, THE SEALED  
DRAWINGS SHALL GOVERN.

BID SET ONLY  
NOT FOR  
CONSTRUCTION  
PRINT DATE: 09/07/22

Jessica Hutchison-Rough, AIA

SHEET  
OF  
E-3  
7

JOB NO.  
022-041A

BF-22-00413



N:\2022\022-041.A - Colton - Lot 15, Pine Canyon\3D\Revit\Drawings\Colton - Camiloli.rvt 9/7/2022 11:32:44 AM



**A.F.C.I.:**  
ALL BRANCH CIRCUITS THAT SUPPLY 120-VOLT, SINGLE-PHASE, 15- AND 20-AMPERE OUTLETS INSTALLED IN FAMILY ROOMS, KITCHENS, DINING ROOMS, LAUNDRY ROOMS, LIVING ROOMS, LIBRARIES, DENS, BEDROOMS, RECREATION ROOMS, CLOSETS, HALLWAYS AND SIMILAR ROOMS OR AREAS SHALL BE PROTECTED BY A COMBINATION TYPE OR BRANCH/FEEDER TYPE ARC-FAULT CIRCUIT INTERRUPTER (AFCI) INSTALLED TO PROVIDE PROTECTION OF THE ENTIRE BRANCH CIRCUIT.

**EXTERIOR LIGHTING:**  
FIXTURES LOCATED OUTSIDE UNDER COVER SHALL BE LISTED FOR DAMP LOCATIONS. ALL OTHER EXTERIOR FIXTURES SHALL BE LISTED FOR WET LOCATIONS - TYP.



**TAMPER-RESISTANT RECEPTACLES:**  
ALL 15 AND 20 AMPERE RECEPTACLES LOCATED IN FAMILY ROOMS, LIBRARIES, DENS, BEDROOMS, SUNROOMS, RECREATION ROOMS, CLOSETS, HALLWAYS AND SIMILAR ROOMS OR AREAS SHALL BE LISTED TAMPER-RESISTANT.

**LIGHTING NOTES:**

- ALL INTERIOR RIB'S NOT SWITCHED SHALL BE ON D/D W/ OVERRIDE SWITCH AND DIMMER @ UTILITY.
- ALL EXTERIOR RIB'S SHALL BE ON D/D.
- ALL RECESSED WALL LIGHTS TO HAVE COMPLETE AND FULL ACCESS TO LIGHT J-BOX
- ALL TRANSFORMERS ARE TO BE UL LISTED AS LIGHTING SYSTEM TRANSFORMERS. ALL LIGHTING TRANSFORMERS MUST MEET REQUIREMENTS ARTICLE 411 OF NATIONAL ELECTRICAL CODE UL-2109/UL-1839.
- A MINIMUM OF 90% OF THE LAMPS IN PERMANENTLY INSTALLED LIGHTING FIXTURES SHALL BE HIGH - EFFICACY LAMPS OR A MINIMUM OF 75% OF THE PERMANENTLY INSTALLED LIGHTING FIXTURES SHALL CONTAIN ONLY HIGH-EFFICACY LAMPS.

| ELECTRICAL SYMBOL LEGEND |                                                                          |
|--------------------------|--------------------------------------------------------------------------|
|                          | SWITCH SINGLE POLE @ 145° A.F.F. UNLESS NOTED OTHERWISE                  |
|                          | 3 WAY SWITCH                                                             |
|                          | 4 WAY SWITCH                                                             |
|                          | SMART SWITCH                                                             |
|                          | DIMMER SWITCH                                                            |
|                          | DOOR JAMB SWITCH                                                         |
|                          | LIGHT, C.L.S. MOUNTED                                                    |
|                          | LIGHT, C.L.S. MOUNTED                                                    |
|                          | LIGHT/WALL MOUNTED @ 140° UNLESS NOTED OTHERWISE                         |
|                          | LIGHT, SURFACE MOUNTED ADJ. SPOT                                         |
|                          | FIRE SPRINKLER ALARM                                                     |
|                          | LIGHT, RECESSED IN CEILING                                               |
|                          | LIGHT, RECESSED IN CEILING (ADJUST.)                                     |
|                          | LIGHT, RECESSED WALL WASHER                                              |
|                          | STRIP LIGHTING                                                           |
|                          | LIGHT RECESSED IN WALL @ 12° UNLESS NOTED OTHERWISE                      |
|                          | FLUORESCENT LIGHT, SURFACE MTD. UNLESS NOTED OTHERWISE                   |
|                          | FLUORESCENT WALL MOUNT (ABOVE DOOR)                                      |
|                          | PLASTER WALL SCONCE @ 10° UNLESS NOTED OTHERWISE                         |
|                          | WEATHER PROOF LIGHT FIXTURE LISTED FOR DAMP LOCATION                     |
|                          | "J-BOX" FLUSH MOUNTED                                                    |
|                          | MULTI SPEED FAN, 2 CIRCUITS, DBL. SWITCH                                 |
|                          | POWERSTRIP IN DRAWER POWER FROM GFCI RECEPTACLE @ 12°                    |
|                          | 110V DUPLEX RECEPTACLE MOUNTED AT POTSHelf LEVEL                         |
|                          | DUPLEX 110V RECEPTACLE @ 12° UNLESS NOTED OTHERWISE                      |
|                          | FOURPLEX 110V RECEPTACLE @ 12° UNO                                       |
|                          | RECEPTACLE @ 12° ONE SIDE SWITCHED                                       |
|                          | 220 VOLT RECEPTACLE                                                      |
|                          | RECEPTACLE WITH GROUND FAULT INTERRUPTER (GFCI), MTD. ABOVE COUNTER      |
|                          | ENTIRE CIRCUIT SHALL BE PROTECTED BY AN ARC-FAULT CIRCUIT INTERRUPTER(S) |
|                          | RECEPTACLE WEATHERPROOF, GFCI                                            |
|                          | CLOCK BOX                                                                |
|                          | GFCI RECEPTACLE RECESSED IN FLOOR, VERIFY LOCATION                       |
|                          | TELEPHONE JACK                                                           |
|                          | PHONE JACK, RECESSED IN FLOOR                                            |
|                          | DATA JACK                                                                |
|                          | CABLE TV JACK                                                            |
|                          | CABLE TV JACK, FLOOR MOUNT                                               |
|                          | PUSH BUTTON/DOOR BELL                                                    |
|                          | CHIME                                                                    |
|                          | EXHAUST FAN TO OUTSIDE, 5 AIR CHANGES/HR. MIN.                           |
|                          | SPEAKER                                                                  |
|                          | THERMOSTAT                                                               |
|                          | GFCI DISCONNECT                                                          |
|                          | SMOKE DETECTOR                                                           |
|                          | DRAPERY POCKET POWER & LOW VOLTAGE CONTROL, VERIFY SWITCHING             |
|                          | SECURITY KEY PAD                                                         |
|                          | ELECTRICAL SES PANEL, FLUSH MOUNT                                        |
|                          | ELECTRICAL SUB PANEL                                                     |
|                          | LOW VOLTAGE TRANSFORMER                                                  |
|                          | LIGHTING CONTROL PANEL                                                   |
|                          | LIGHTING ZONE                                                            |
|                          | LIGHTING CONTROL KEYPAD                                                  |
|                          | LIGHTING CONTROL, MULTIPLE KEYPADS                                       |
|                          | CARBON MONOXIDE DETECTOR                                                 |
|                          | INTERCOM SYSTEM                                                          |
|                          | REMOTE EXHAUST FAN W/ GRILLE NEAR FLOOR                                  |
|                          | CEILING MOUNTED EXHAUST FAN                                              |
|                          | EXHAUST FAN ON ROOF                                                      |
|                          | DUSK TO DAWN PHOTOCCELL                                                  |
|                          | POT SHELF                                                                |
|                          | TOE KICK                                                                 |
|                          | UNDER COUNTER                                                            |
|                          | WATER PROOF FIXTURE                                                      |
|                          | DAMP PROOF FIXTURE                                                       |
|                          | AUTOMATIC GARAGE DOOR OPENER                                             |
|                          | HOME RUN TO LIGHTING CONTROL SYSTEM                                      |
|                          | INFRARED HEATER 220V                                                     |

UPPER LEVEL LIGHTING PLAN

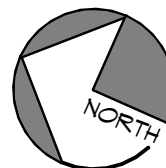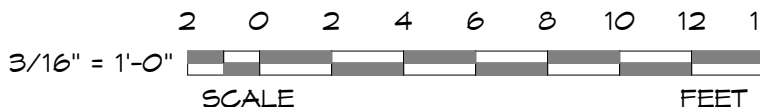

A CUSTOM RESIDENCE PREPARED FOR  
MR. & MS. COLTON  
LOT #15

**URBAN DESIGN architecture**  
**ASSOCIATES LTD. AIA** 480-905-1212  
8150 N. 86TH. PLACE SCOTTSDALE, ARIZONA 85258

BID SET ONLY  
NOT FOR  
CONSTRUCTION  
PRINT DATE: 09/07/22

DATE: 09/07/22  
DWG BY: BO/CP  
REVISIONS:  
04/14/22 C.O.F. A  
05/17/22 C.O.F. A

ALL IDEAS, REVIEWS AND FINISHES  
REPRESENTED BY THESE DRAWINGS  
ARE THE PROPERTY OF THE  
ARCHITECT AND WILL BE KEPT  
CONFIDENTIAL. NO PARTS MAY  
BE REPRODUCED OR COPIED  
WITHOUT THE WRITTEN  
CONSENT OF THE ARCHITECT.  
THESE DRAWINGS ON THIS PROJECT  
ARE THE PROPERTY OF THE ARCHITECT  
AND WILL BE KEPT CONFIDENTIAL.  
THE USER'S SOLE RISK AND WITHOUT  
LIABILITY TO URBAN DESIGN ASSOC.,  
LTD. IN THE EVENT OF ANY  
ELECTRONIC FILES, THE SEALED  
DRAWINGS SHALL GOVERN.

SHEET  
E-4

OF  
7

JOB NO.  
022-041.A

BF-22-00413

Jessica Hutchison-Rough, AIA